


Projet: LABORATOIRE SOUTERRAIN DE BURE Site: GHA Axe: AXE GHA PC: 123-Profiles extrados INF

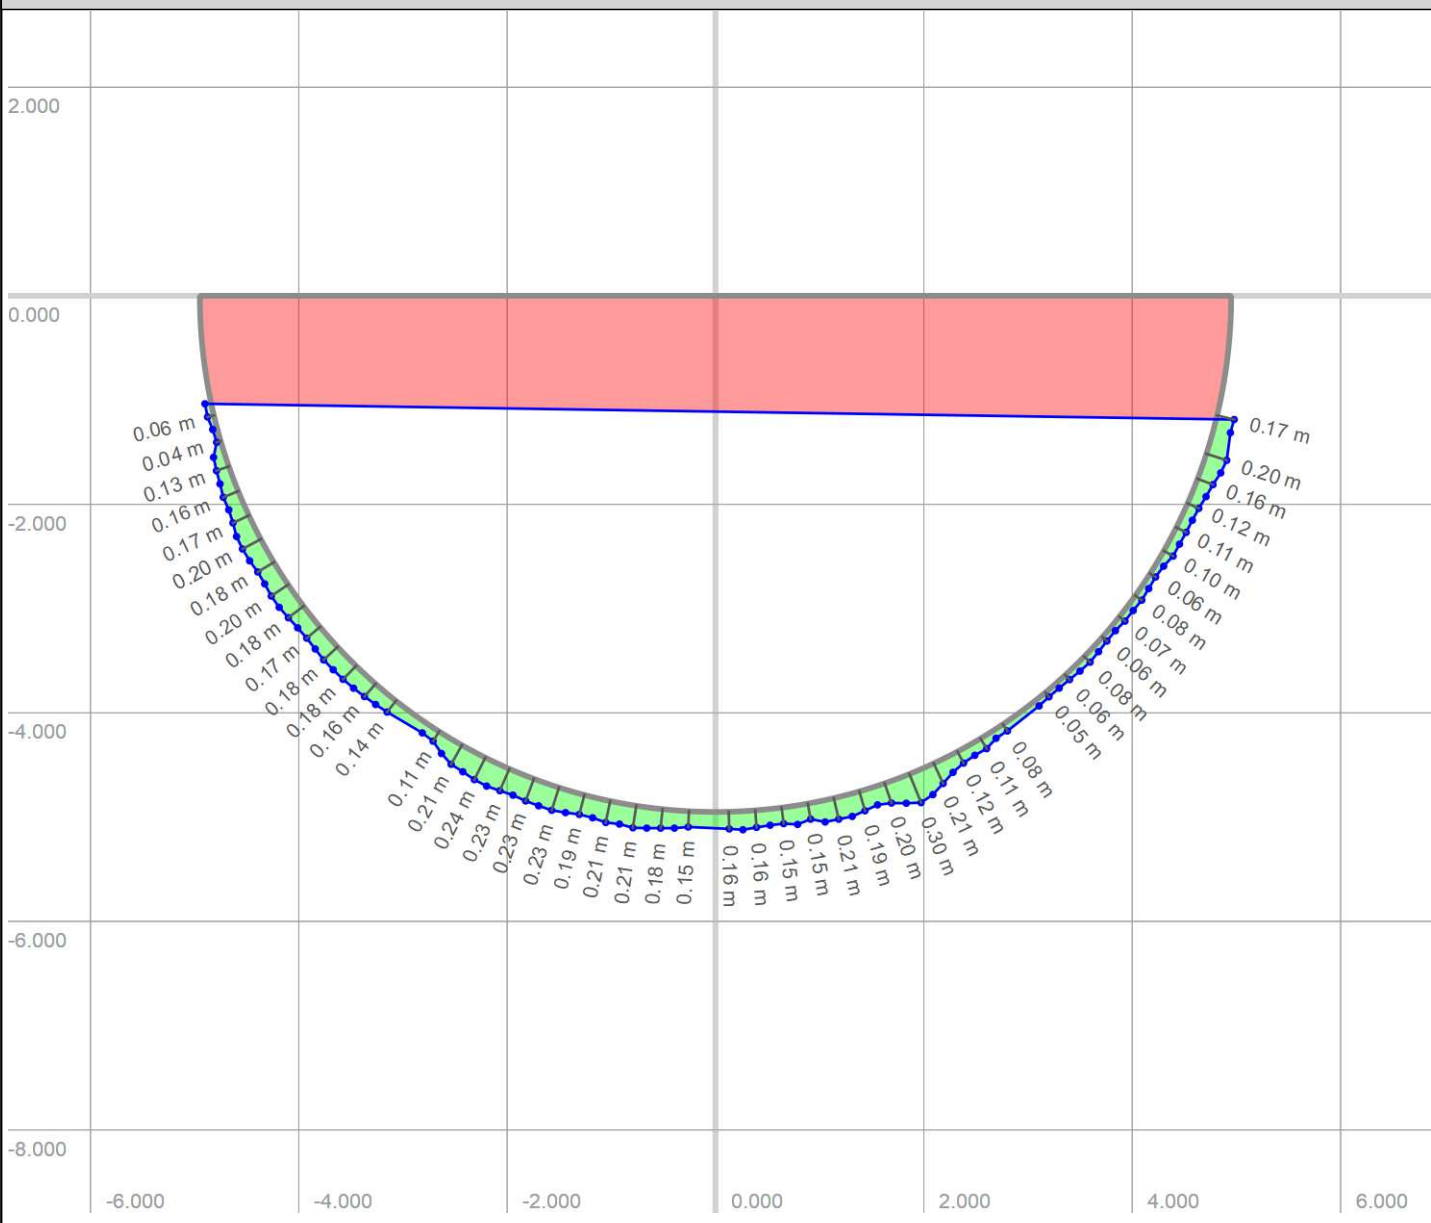

S: 1:72
HD: PM croissant
PC: Vertical



HS: 33.00 m
TM: 33.00 m
PM: N/A

ANDRA - Centre
Meuse/Haute-Marne
RD 960 BURE

123-Profil sur Extrados (INF)

HS: 33.00 m

Mesure

Topographe: C43-INF
Date de mesure: 05/11/2025 9h51
Instrument: 5010X (5010X)
Profil: GHA-T43-leve extrados cale
Bloc: N/A

En cours

Aire mesurée: 29.64 m²
Zone de profil de référence: 38.48 m²
Zone en sous profil: 10.90 m²
Aire en surprofil: 2.05 m²
Circonférence mes.: 23.808 m
Déviation moyenne: 0.15 m

Design data of construction stages

Référence CS	Profil théorique	Pente transv.
■ 123-Profiles extrados IN	410-profil Béton inf	0.0 %

Remarques